




Pt50 (G Pt25 , G Pt6)

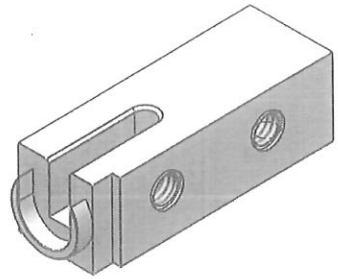

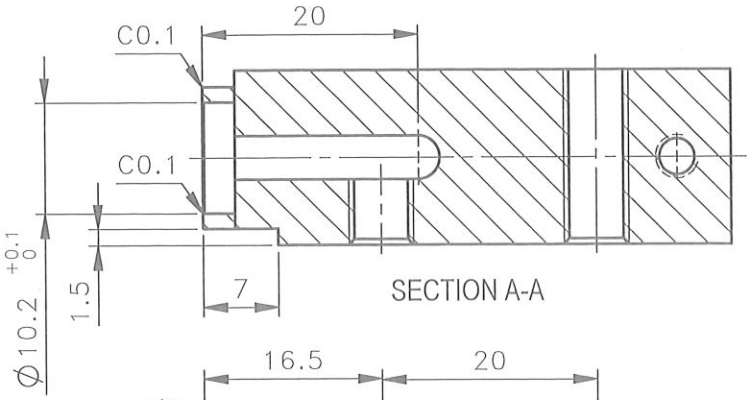

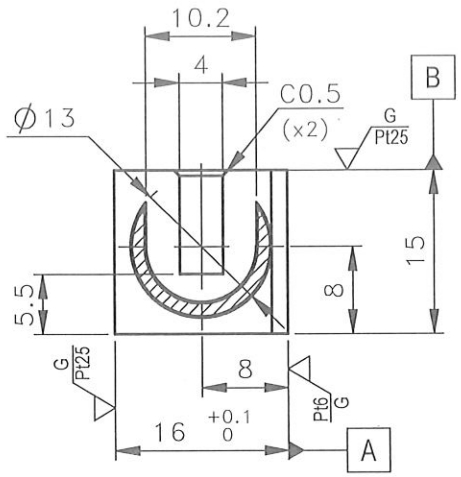

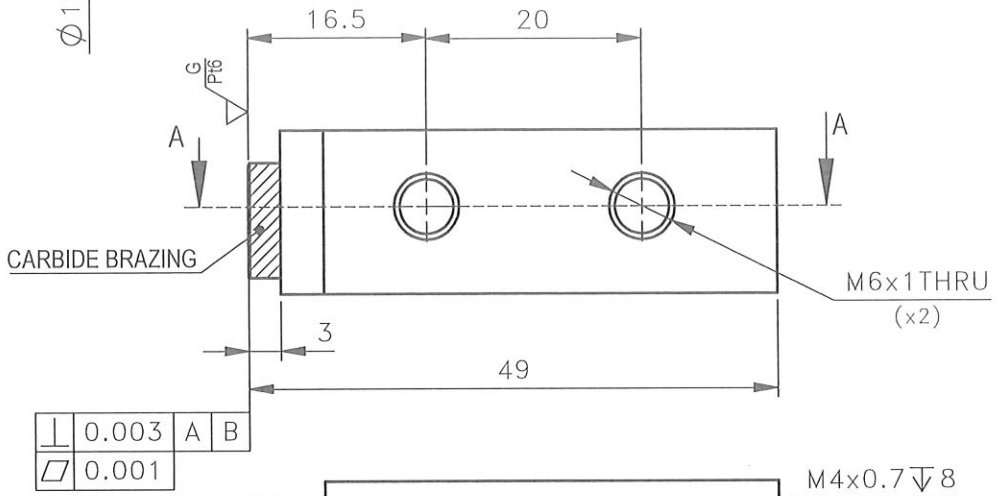

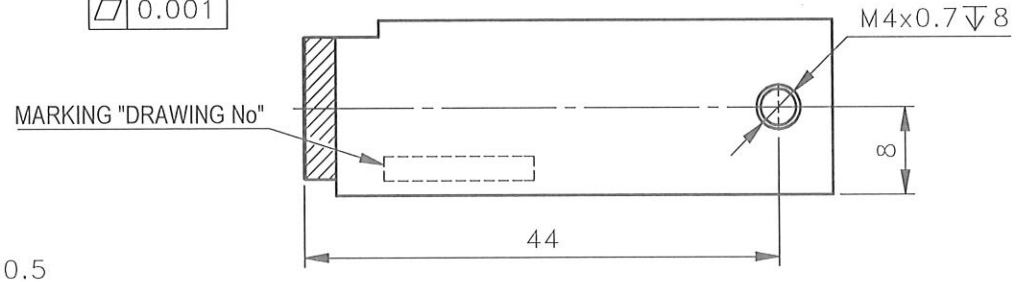

NOTE : 1.CARBIDE GRADE IS EQUIVALENT TO JIS V1.
2.UNLESS OTHERWISE SPECIFIED ALL CORNERS IS C0.5

PMA ENGINEERING
Registration date
4 Mar"25
NMB MinebeaMitsumi Inc.
Precision Mechanical Component Division

REV.	ECN. NO.	DATE	DESCRIPTION	NAME
			-	

BLANK/INSERT TIP No. -
MAKER. -

~~UNLESS SPECIFIED C0.2 or R0.2~~
~~FREE BURR & DENT~~

GENERAL TOLERANCE		Surface
LESS THAN 0.5	±0.05	0.8S
0.5 - 6	±0.1	6S
OVER 6 - 30	±0.2	25S
OVER 30 - 120	±0.3	100S
OVER 120	±0.5	UNCUT
ANGLE	±1°	

FOR MACHINE: TO-50
MATERIAL: S45C,CARBIDE
HEAT TREATMENT: -
SURFACE COATING: -

DESIGN FOR PART No.: OT-7185A
REFER DRAWING No.: LD-MB14-W-02-01
SCALE: 1.5/1 | SHEET: 1 / 1 | UNIT : mm.
PREPARED: WORAWUT | CHECKED: Jirapat | APPROVED: Atty
DATE 28 FEB '2025

3rd. ANGLE

NMB MinebeaMitsumi Inc.
Precision Mechanical Component Division

DRAWING NAME: BACKING
DRAWING NO.: TPMA-35-046
REV.: NR

SIZE A4